


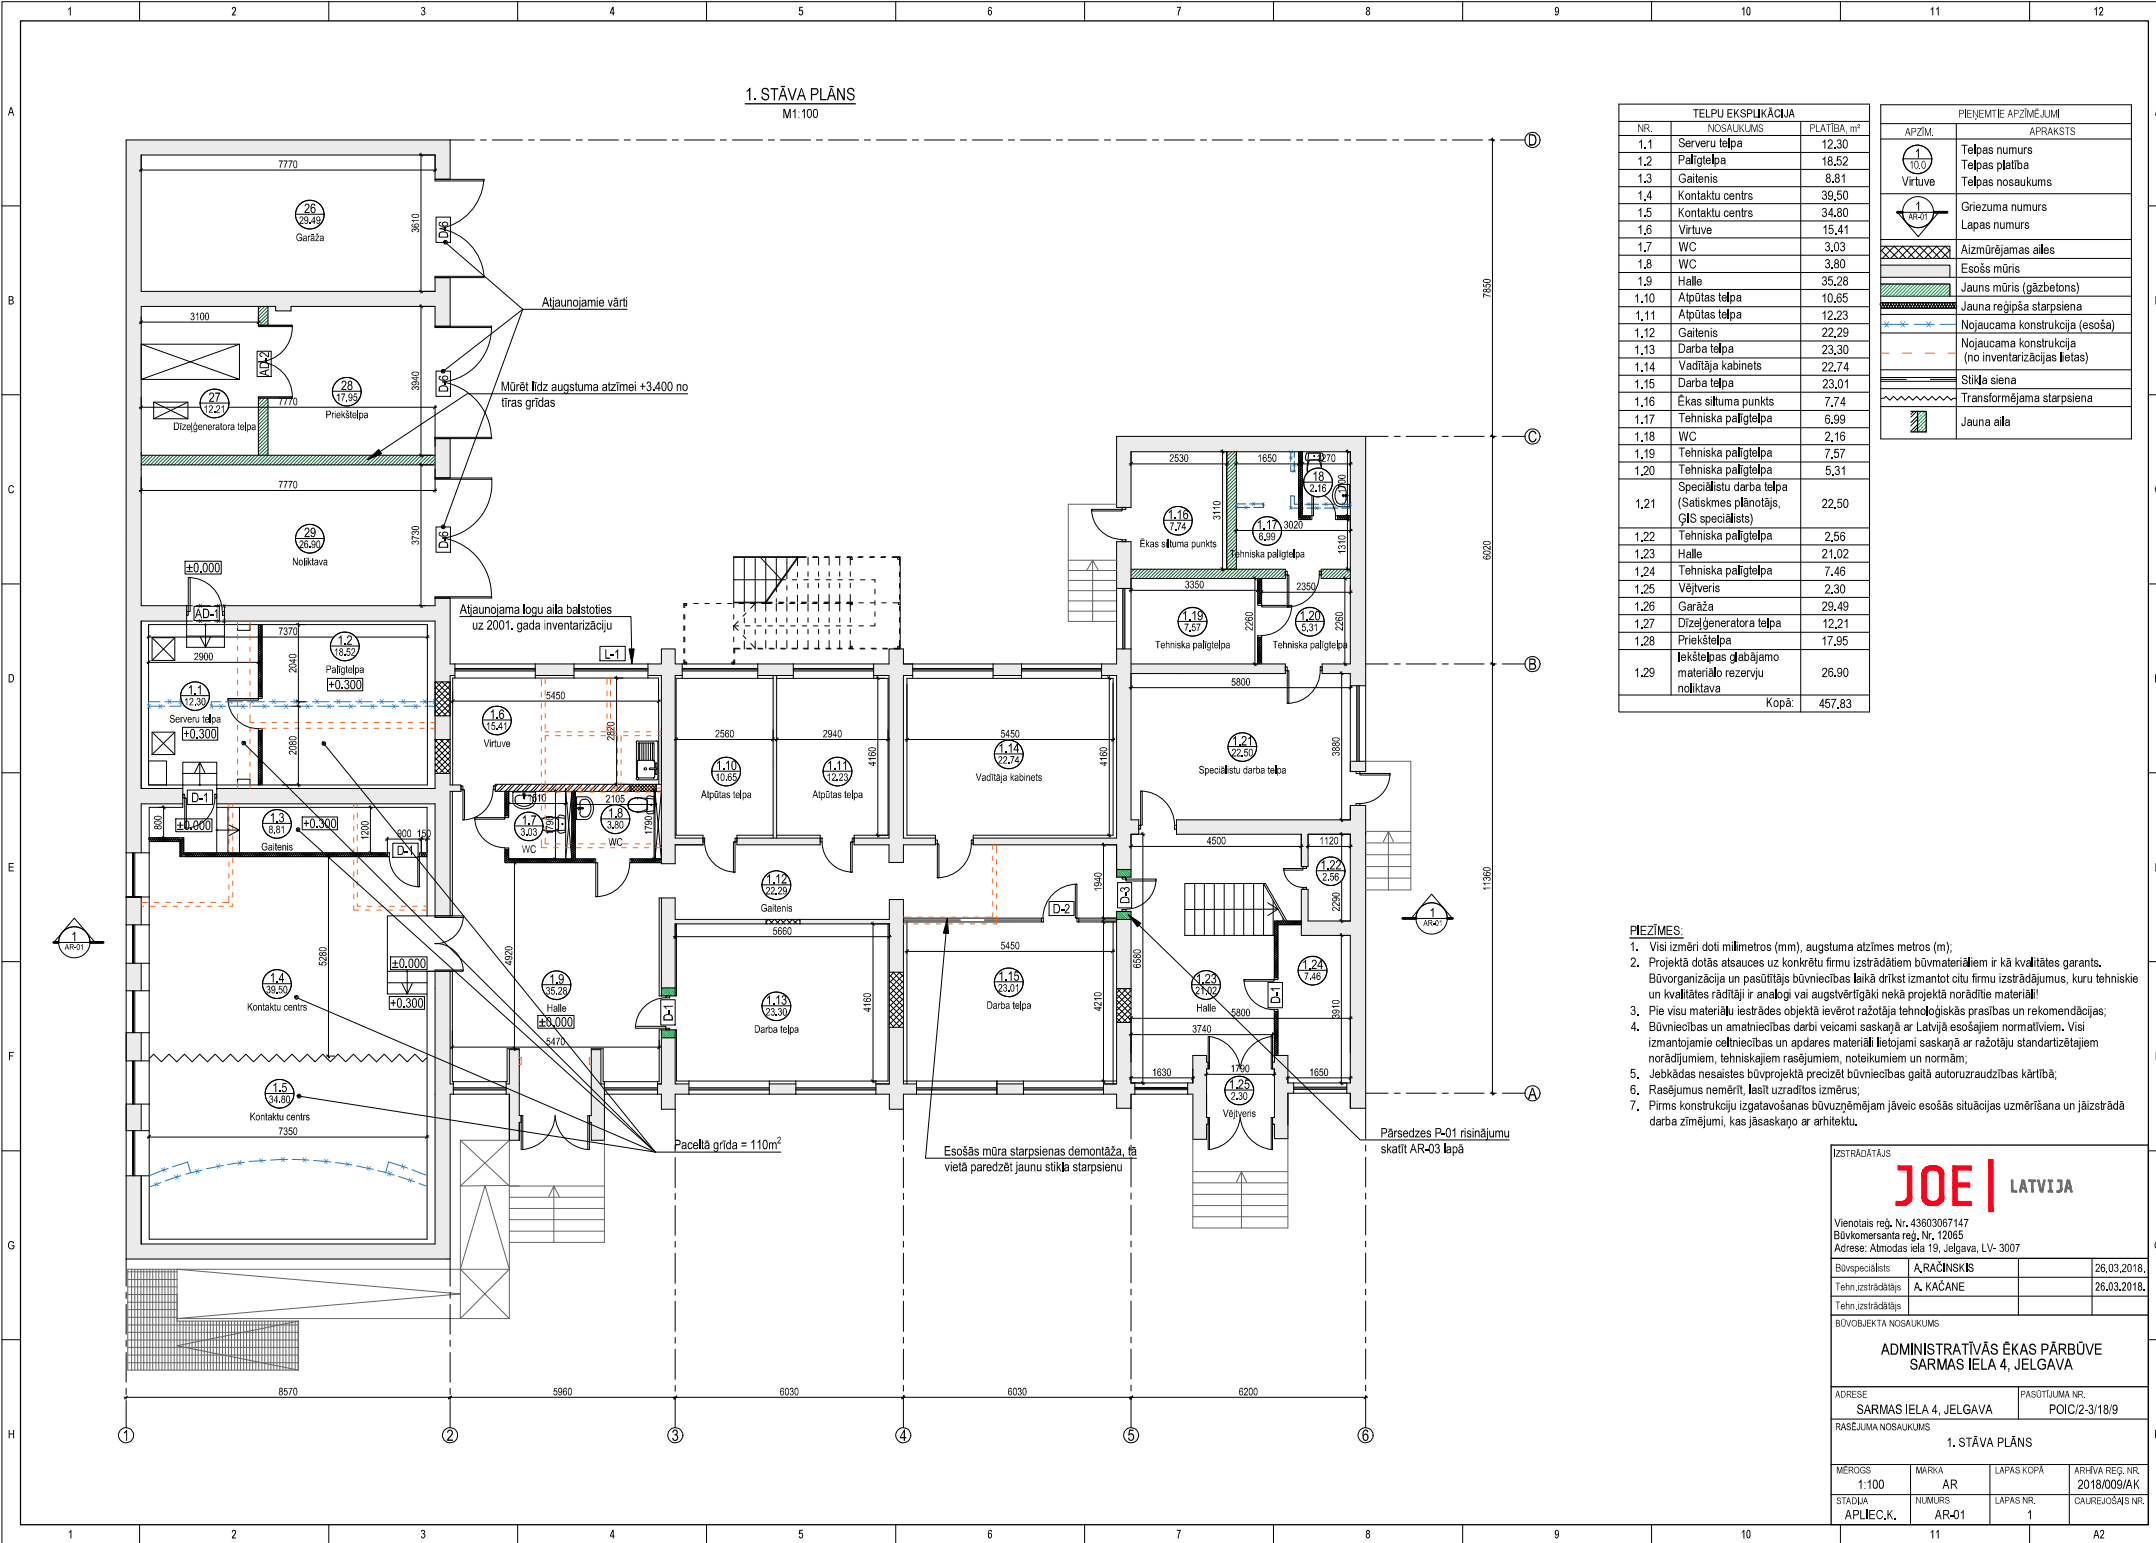

TĒLPU EKSPĻŪKĀCIJA		
NR.	NOSAUKUMS	PLATĪBA, m²
1.1	Serveru telpa	12,30
1.2	Priekštelpa	18,52
1.3	Gaitenis	8,81
1.4	Kontaktu centrs	39,50
1.5	Kontaktu centrs	34,80
1.6	Virtuve	15,41
1.7	WC	3,03
1.8	WC	3,80
1.9	Halle	35,28
1.10	Atpūtas telpa	10,65
1.11	Atpūtas telpa	12,23
1.12	Gaitenis	22,29
1.13	Darba telpa	23,30
1.14	Vadītāja kabinets	22,74
1.15	Darba telpa	23,01
1.16	Ēkas siltuma punkts	7,74
1.17	Tehniska palīgtelpa	6,99
1.18	WC	2,16
1.19	Tehniska palīgtelpa	7,57
1.20	Tehniska palīgtelpa	5,31
1.21	Speciālistu darba telpa (Saviesības plānoja, (JIS speciālists)	22,50
1.22	Tehniska palīgtelpa	2,56
1.23	Halle	21,02
1.24	Tehniska palīgtelpa	7,46
1.25	Vēlītveris	2,30
1.26	Garāža	29,49
1.27	Dizelģenerators telpa	12,21
1.28	Priekštelpa	17,95
1.29	Iekšējās glabājamo materiālu rezervju noliktava	26,90
Kopā:		457,83

PIENĒMIE APZĪMĒJUMI	
APZĪM.	APRAKSTS
	Telpas numurs
	Telpas platība
	Telpas nosaukums
	Griezuma numurs
	Lapas numurs
	Aizmūrējamas ailes
	Esošs mūris
	Jauns mūris (gāzbetons)
	Jauna režģisā starpsiena
	Nojaukama konstrukcija (esoša)
	Nojaukama konstrukcija (no inventarizācijas lietās)
	Stikla siena
	Transformējama starpsiena
	Jauna aila

- PIEZĪMES:**
- Visi izmēri doti milimetros (mm), augstuma atzīmes metros (m);
 - Projekta dotās atsaucies uz konkrētu firmu izstrādātiem būvmateriāliem ir kā kvalitātes garants. Būvorganizācija un pasūtītājs būvniecības laikā drīkst izmantot citu firmu izstrādājumus, kuru tehniskie un kvalitātes rādītāji ir analogi vai augstvērtīgāki nekā projektā norādītie materiāli;
 - Pie visu materiālu iestādes objektā jāievēro ražotāja tehniskās prasības un rekomendācijas;
 - Būvniecības un amatniecības darbi veicami saskaņā ar Latvijā esošajiem normatīviem. Visi izmantotie būvniecības un apdreses materiāli jābūt saskaņā ar ražotāju standartizētajiem norādījumiem, tehniskajiem rasējumiem, noteikumiem un normām;
 - Jebkādas nesācīgas būvprojekta precizēt būvniecības laikā autoruzraudzības kārtībā;
 - Rasījumus nemēri, kas uzradītos izstrādā;
 - Pirms konstrukciju izgatavošanas būvuzņēmējam jāveic esošās situācijas uzmēršana un jāizstrādā darba zīmējumi, kas jānosaka ar arhitektu.

IZSTRĀDĀTĀJS

JOE | LATVIJA

Vienotais reģ. Nr. 43603067147
Būvkomersanta reģ. Nr. 12065
Adrese: Almodas iela 18, Jelgava, LV- 3007

Būvspeciālists
Tehn. izstrādātājs

A. RAČĪNSKIS
A. KAČANE

26.03.2018.
26.03.2018.

BŪVOBJEKTA NOSAUKUMS

ADMINISTRATĪVĀS ĒKAS PĀRBŪVE
SARMAS IELA 4, JELGAVA

ADRESE
SARMAS IELA 4, JELGAVA

PASŪTĪJUMA NR.
POIC/2-3/18/9

1. STĀVA PLĀNS

MĒROGS
1:100

MARKA
AR

LAPAS KOPĀ
**ARHIVA REĢ. NR.
2018/009/AK**

STADIJA
APLIECĶ.

NUMURS
AR-01

LAPAS NR.
1

CAURĒJOTĀJS NR.
2018/009/AK

